

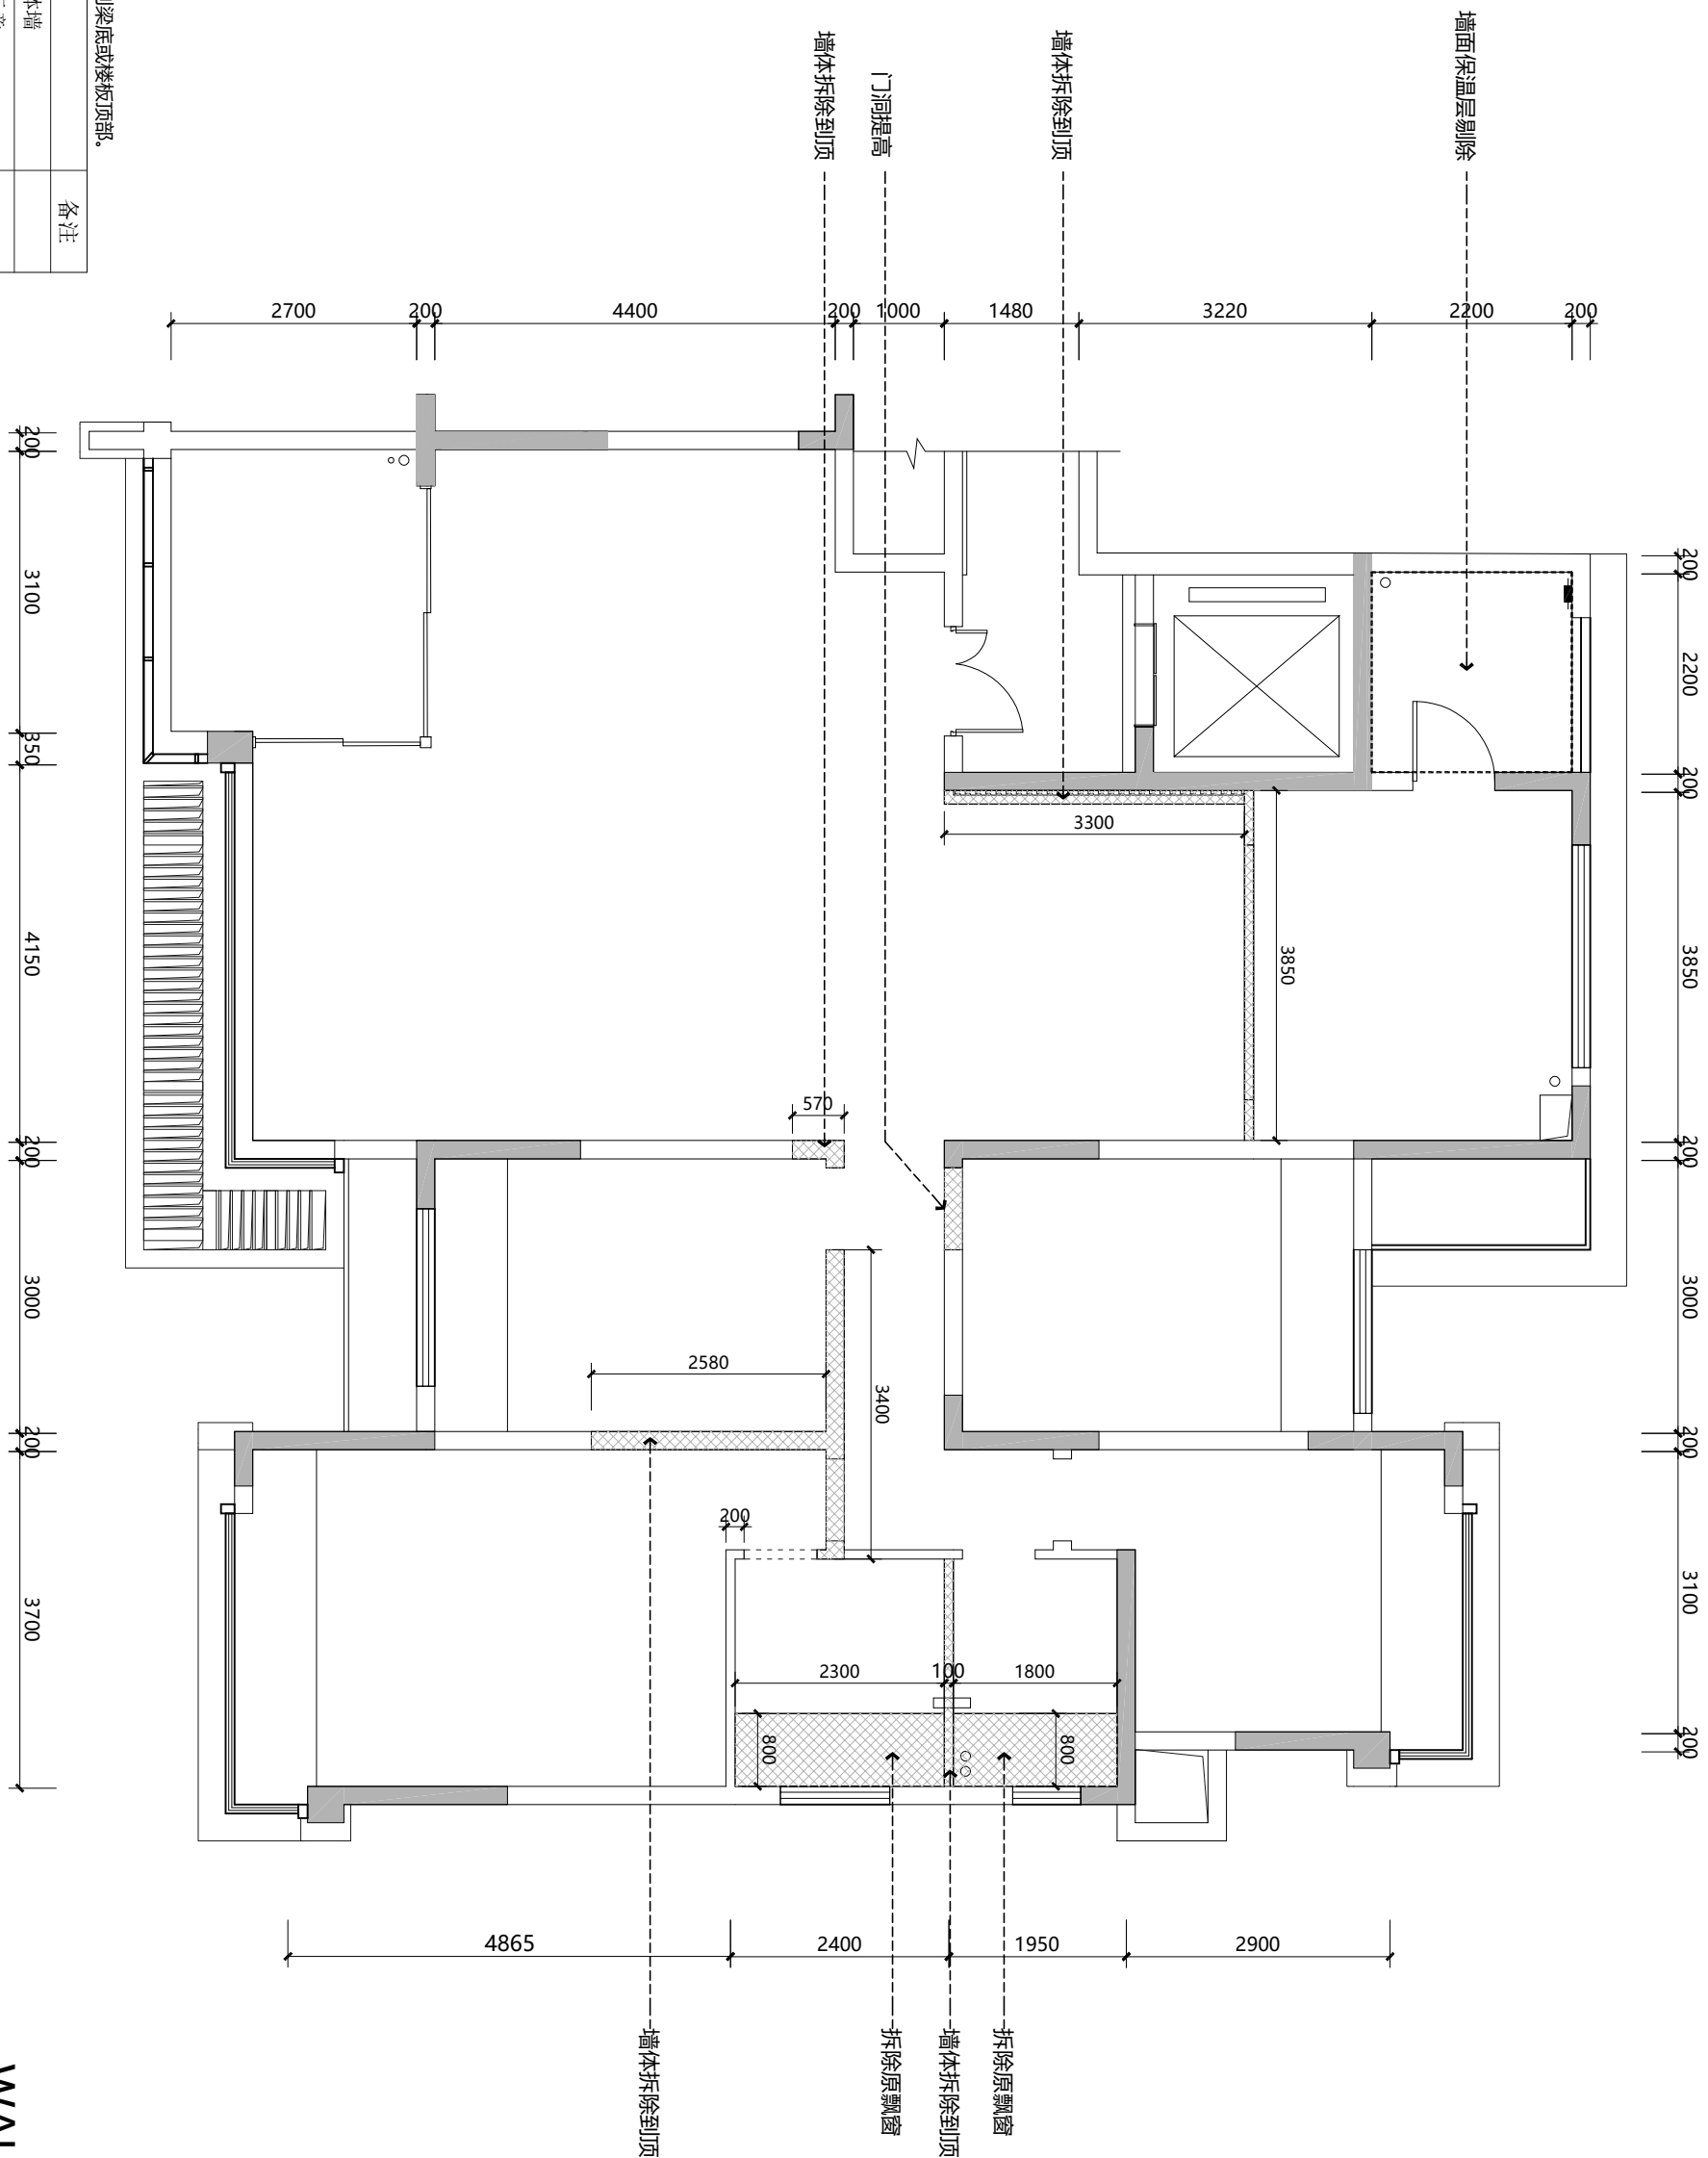


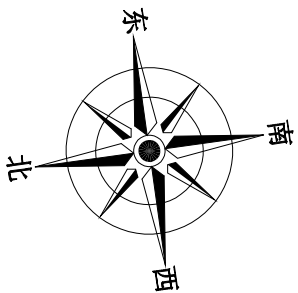

图例	说明	备注
	原建筑墙体	
	拆除墙体示意	
	新建轻质砖	
	现浇楼板 (由专业厂家设计配筋图并施工)	

注: 除特殊标注外, 其余所有墙体全部拆除到梁底或楼板顶部。

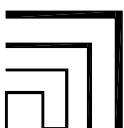

YS
STUDIO

地址：重庆市渝北区食品城大道创意公园4期17幢1单元2A

工程名稱 PROJECT	編號 JOB NO	比例 SCALE	繪圖 DRAWN BY
昱湖壹号萃峯17-1-1502		1:80	
圖稱 TITLE	日期 DATE	單位 UNIT	設計 DESIGNED BY
拆除墙体圖	2025/2		楊相立
		核准 APPROVED BY	

[illegible]

WALL DIMENSION PLAN 拆除墙体图	SCALE 1:80
---	--

頁數 NUMBER
版權所有
請尊重智慧財產

