

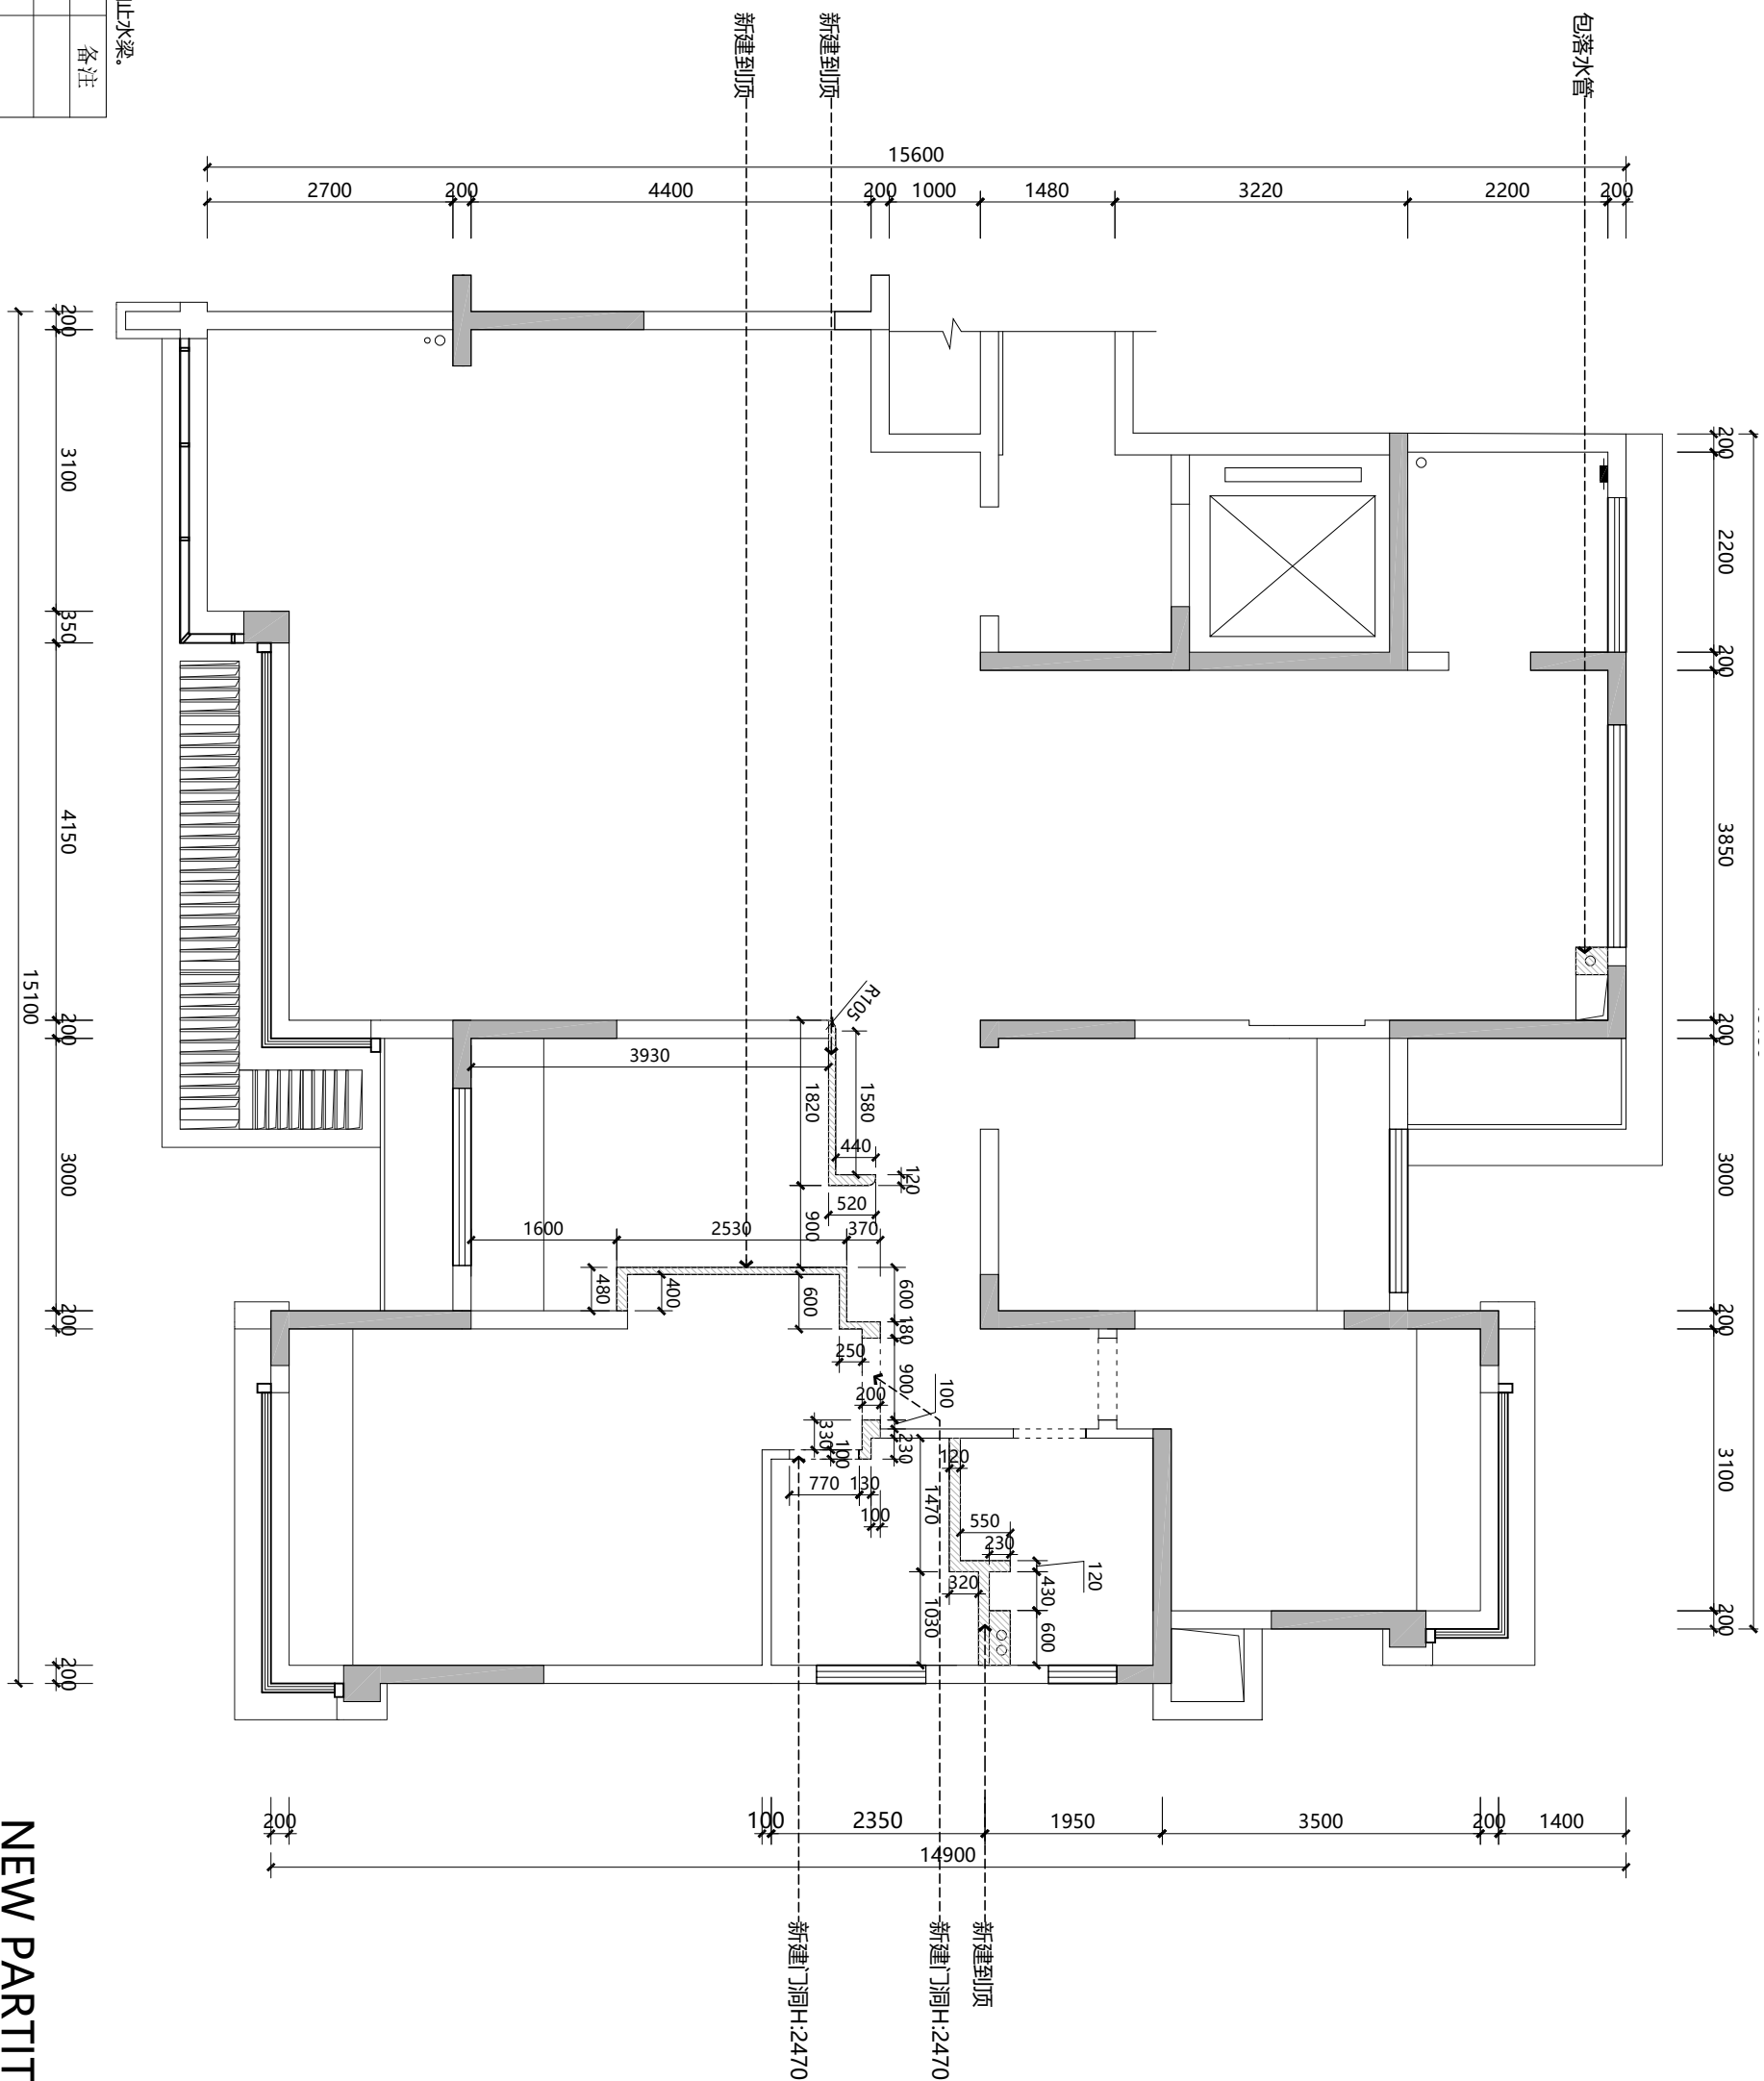


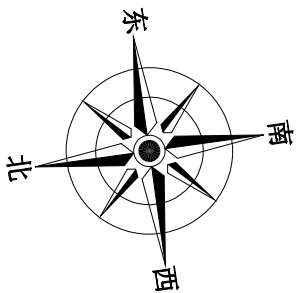

图例	说明	备注
	原建筑砌体墙	
	拆除墙体示意	
	新建轻质砖	
	现浇楼板 (由专业厂家设计配筋图并施工)	

注：所有墙体全部到顶，门过梁统一高度2470，厨卫新建墙需增加止水梁。

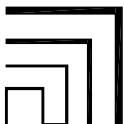

YS
STUDIO

地址：重庆市渝北区食品城大道创意公园4期17幢1单元2A

工程名稱 PROJECT	編號 JOB NO	比例 SCALE	繪圖 DRAWN BY
昱湖壹号萃峯17-1-1502		1:80	
圖稱 TITLE	日期 DATE	單位 UNIT	設計 DESIGNED BY
新建墙体图	2025/2		大宇 杨旭
			核准 APPROVED BY

兰银杨芳

核准 APPROVED BY

圖面修正 次列NO.	日期DATE	修改內容REVISION	圖號	DRAWING NO.

PL-03

頁數 NUMBER

版權所有
請尊重智慧財產權



NEW PARTITION WALL PLAN

新建墙体图

SCALE 1:80

SCALE 1:80