



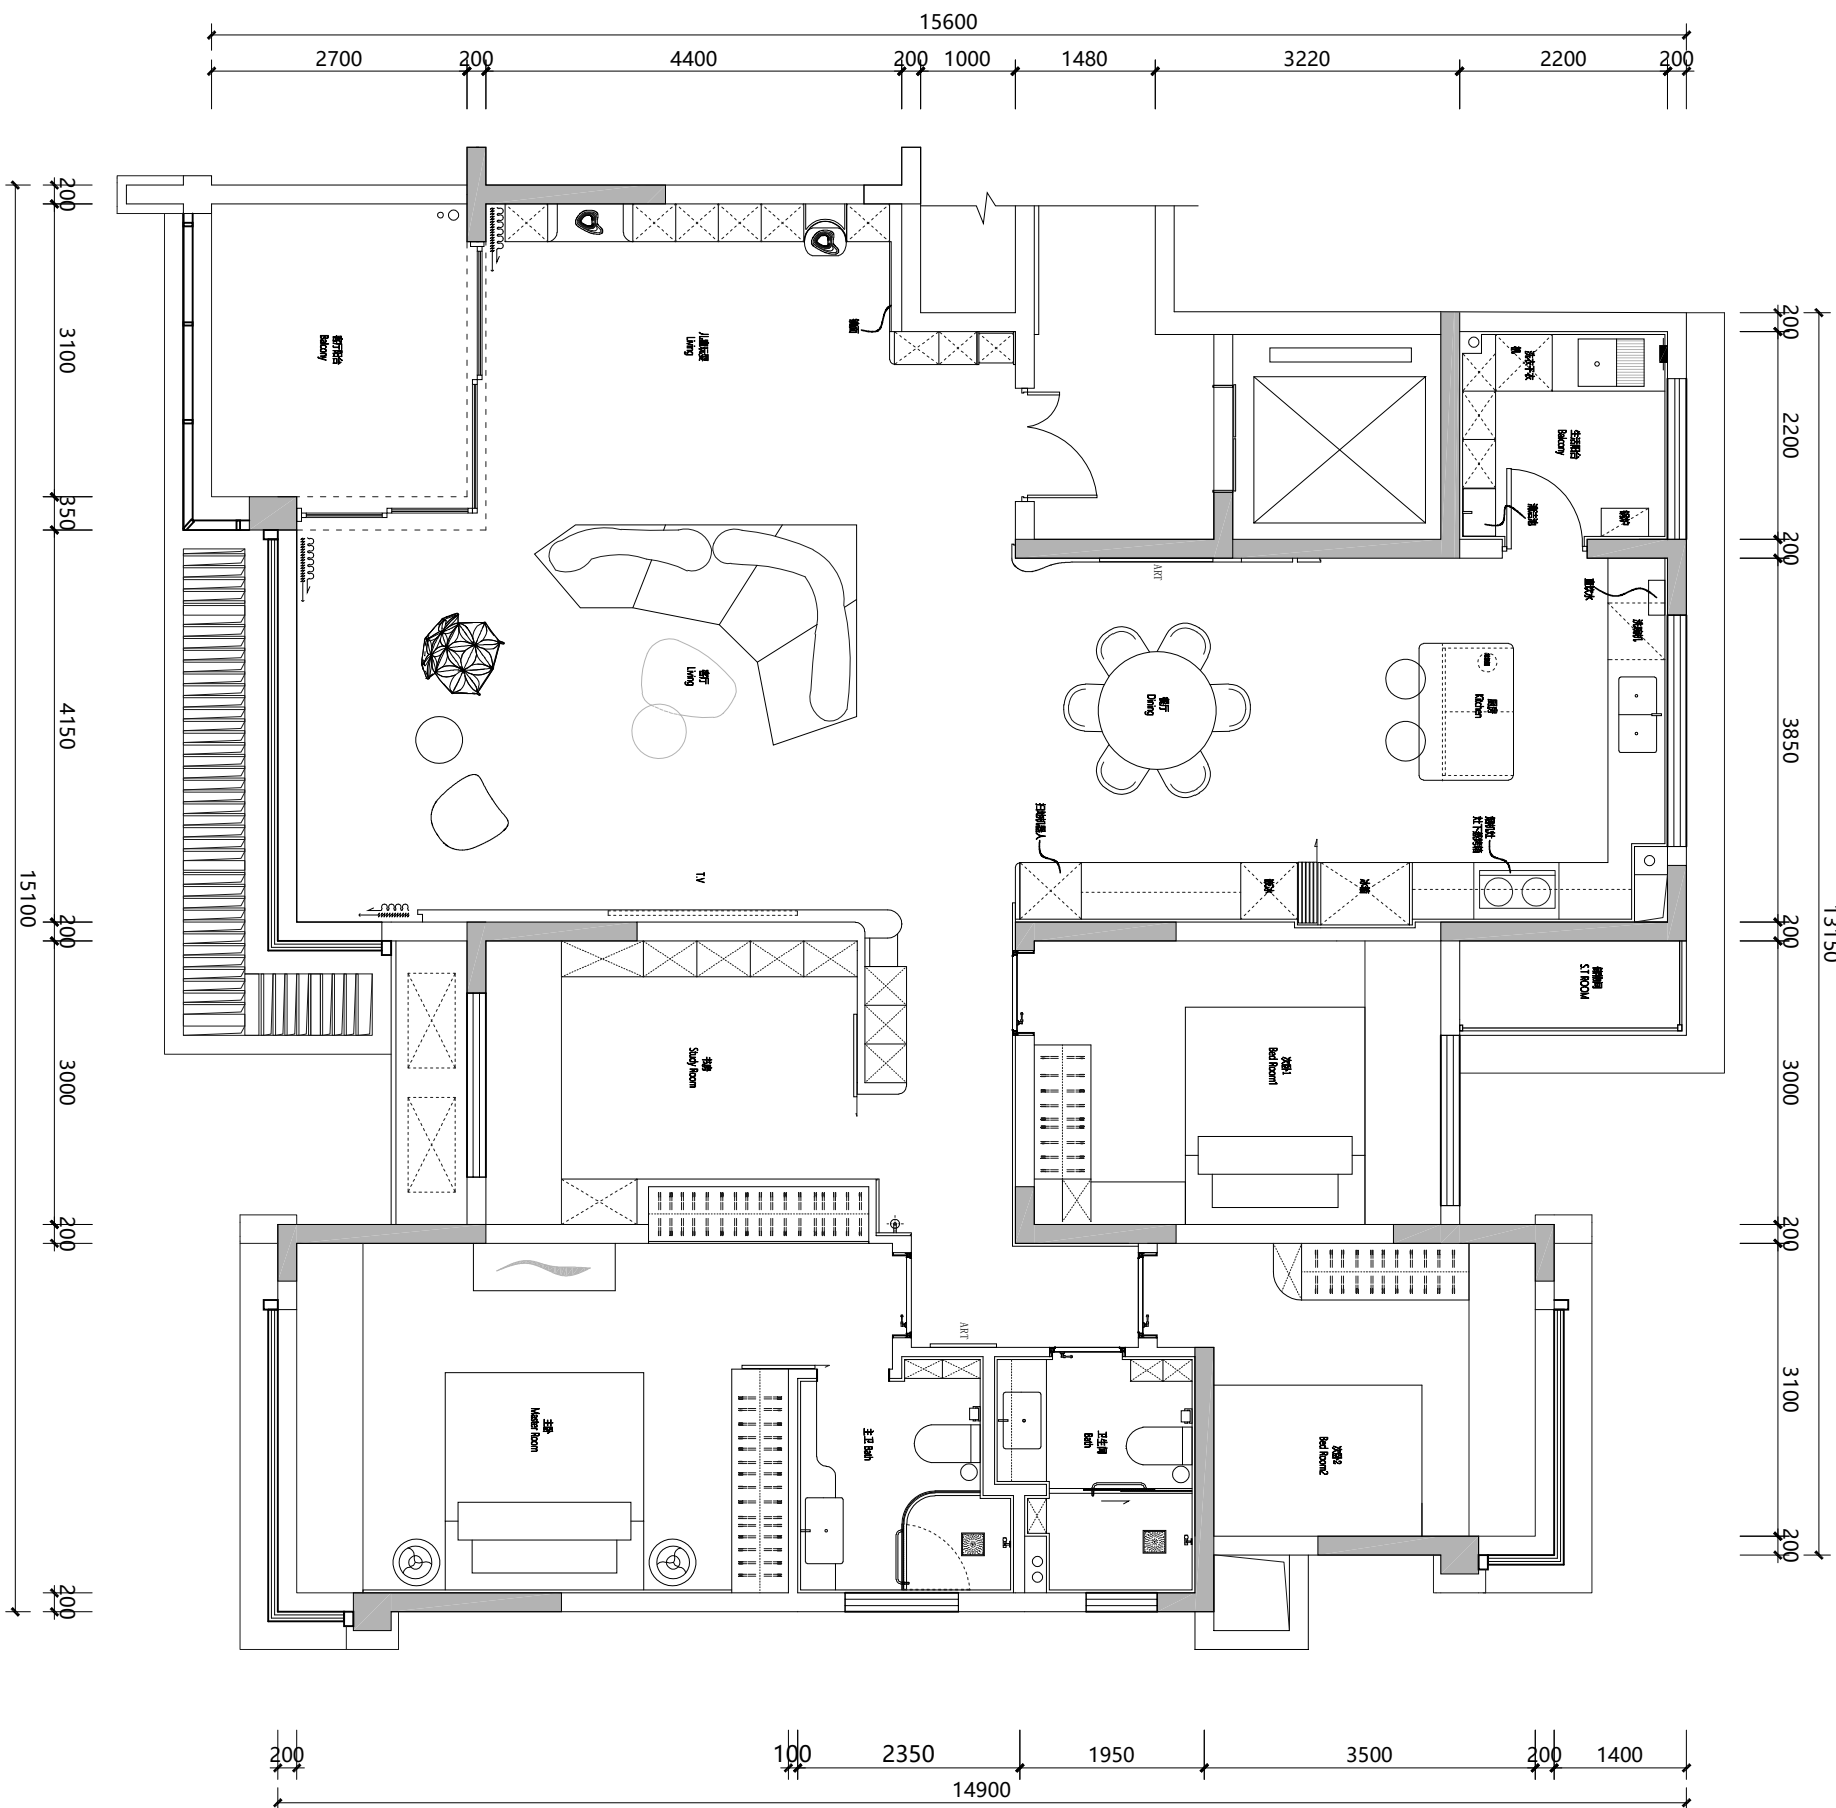

平面布置图
SCALE 1:80

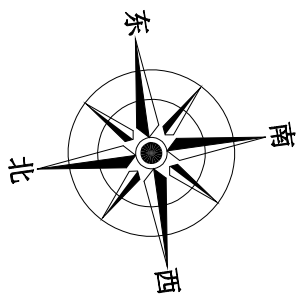

YS STUDIO
地址：重庆市渝北区食品城大道创意公园4期17幢1单元2A

工程名稱 PROJECT	昱湖壹号萃萃17-1-1502	編號 JOB NO	2025/2	單位 UNIT	1:80	繪圖 DRAWN BY	楊銀蘭	圖面修正 次別NO.	日期DATE	修改內容REVISION	圖號 DRAWING NO.
圖稱 TITLE	平面布置图	日期 DATE	2025/2	單位 UNIT	1:80	設計 DESIGNED BY	楊銀蘭	核准 APPROVED BY			PL-04

圖面修正 次別NO.	日期DATE	修改內容REVISION	圖號 DRAWING NO.	頁數 NUMBER
				版權所有 請尊重智慧財產權

