


注：开关高度为完成面高度

序号	图例	名称	类别	安装高度
1		单联单控开关	86型	下口离地1250MM
2		双联单控开关	86型	下口离地1250MM
3		三联单控开关	86型	下口离地1250MM
4		单联双控开关	86型	下口离地1250MM
5		双联双控开关	86型	下口离地1250MM
6		浴霸开关	86型	下口离地1250MM
7		人体感应开关	/	天花嵌装

编号	块缩略图	名称	说明
R1		LED灯带	5W/米/3500K
R2		壁灯	10W/3500K
R3		吊灯	20W/3500K
R4		明装射灯	7W/3500K
R5		深杯防眩光可调射灯	100MM*200MM/7W/3500K
R6		深杯防眩射灯	7W/3500K
R7		暖风机	-
R8		空调出风口	-
R9		空调回风口	-
R10		吸顶灯	10W/3500K

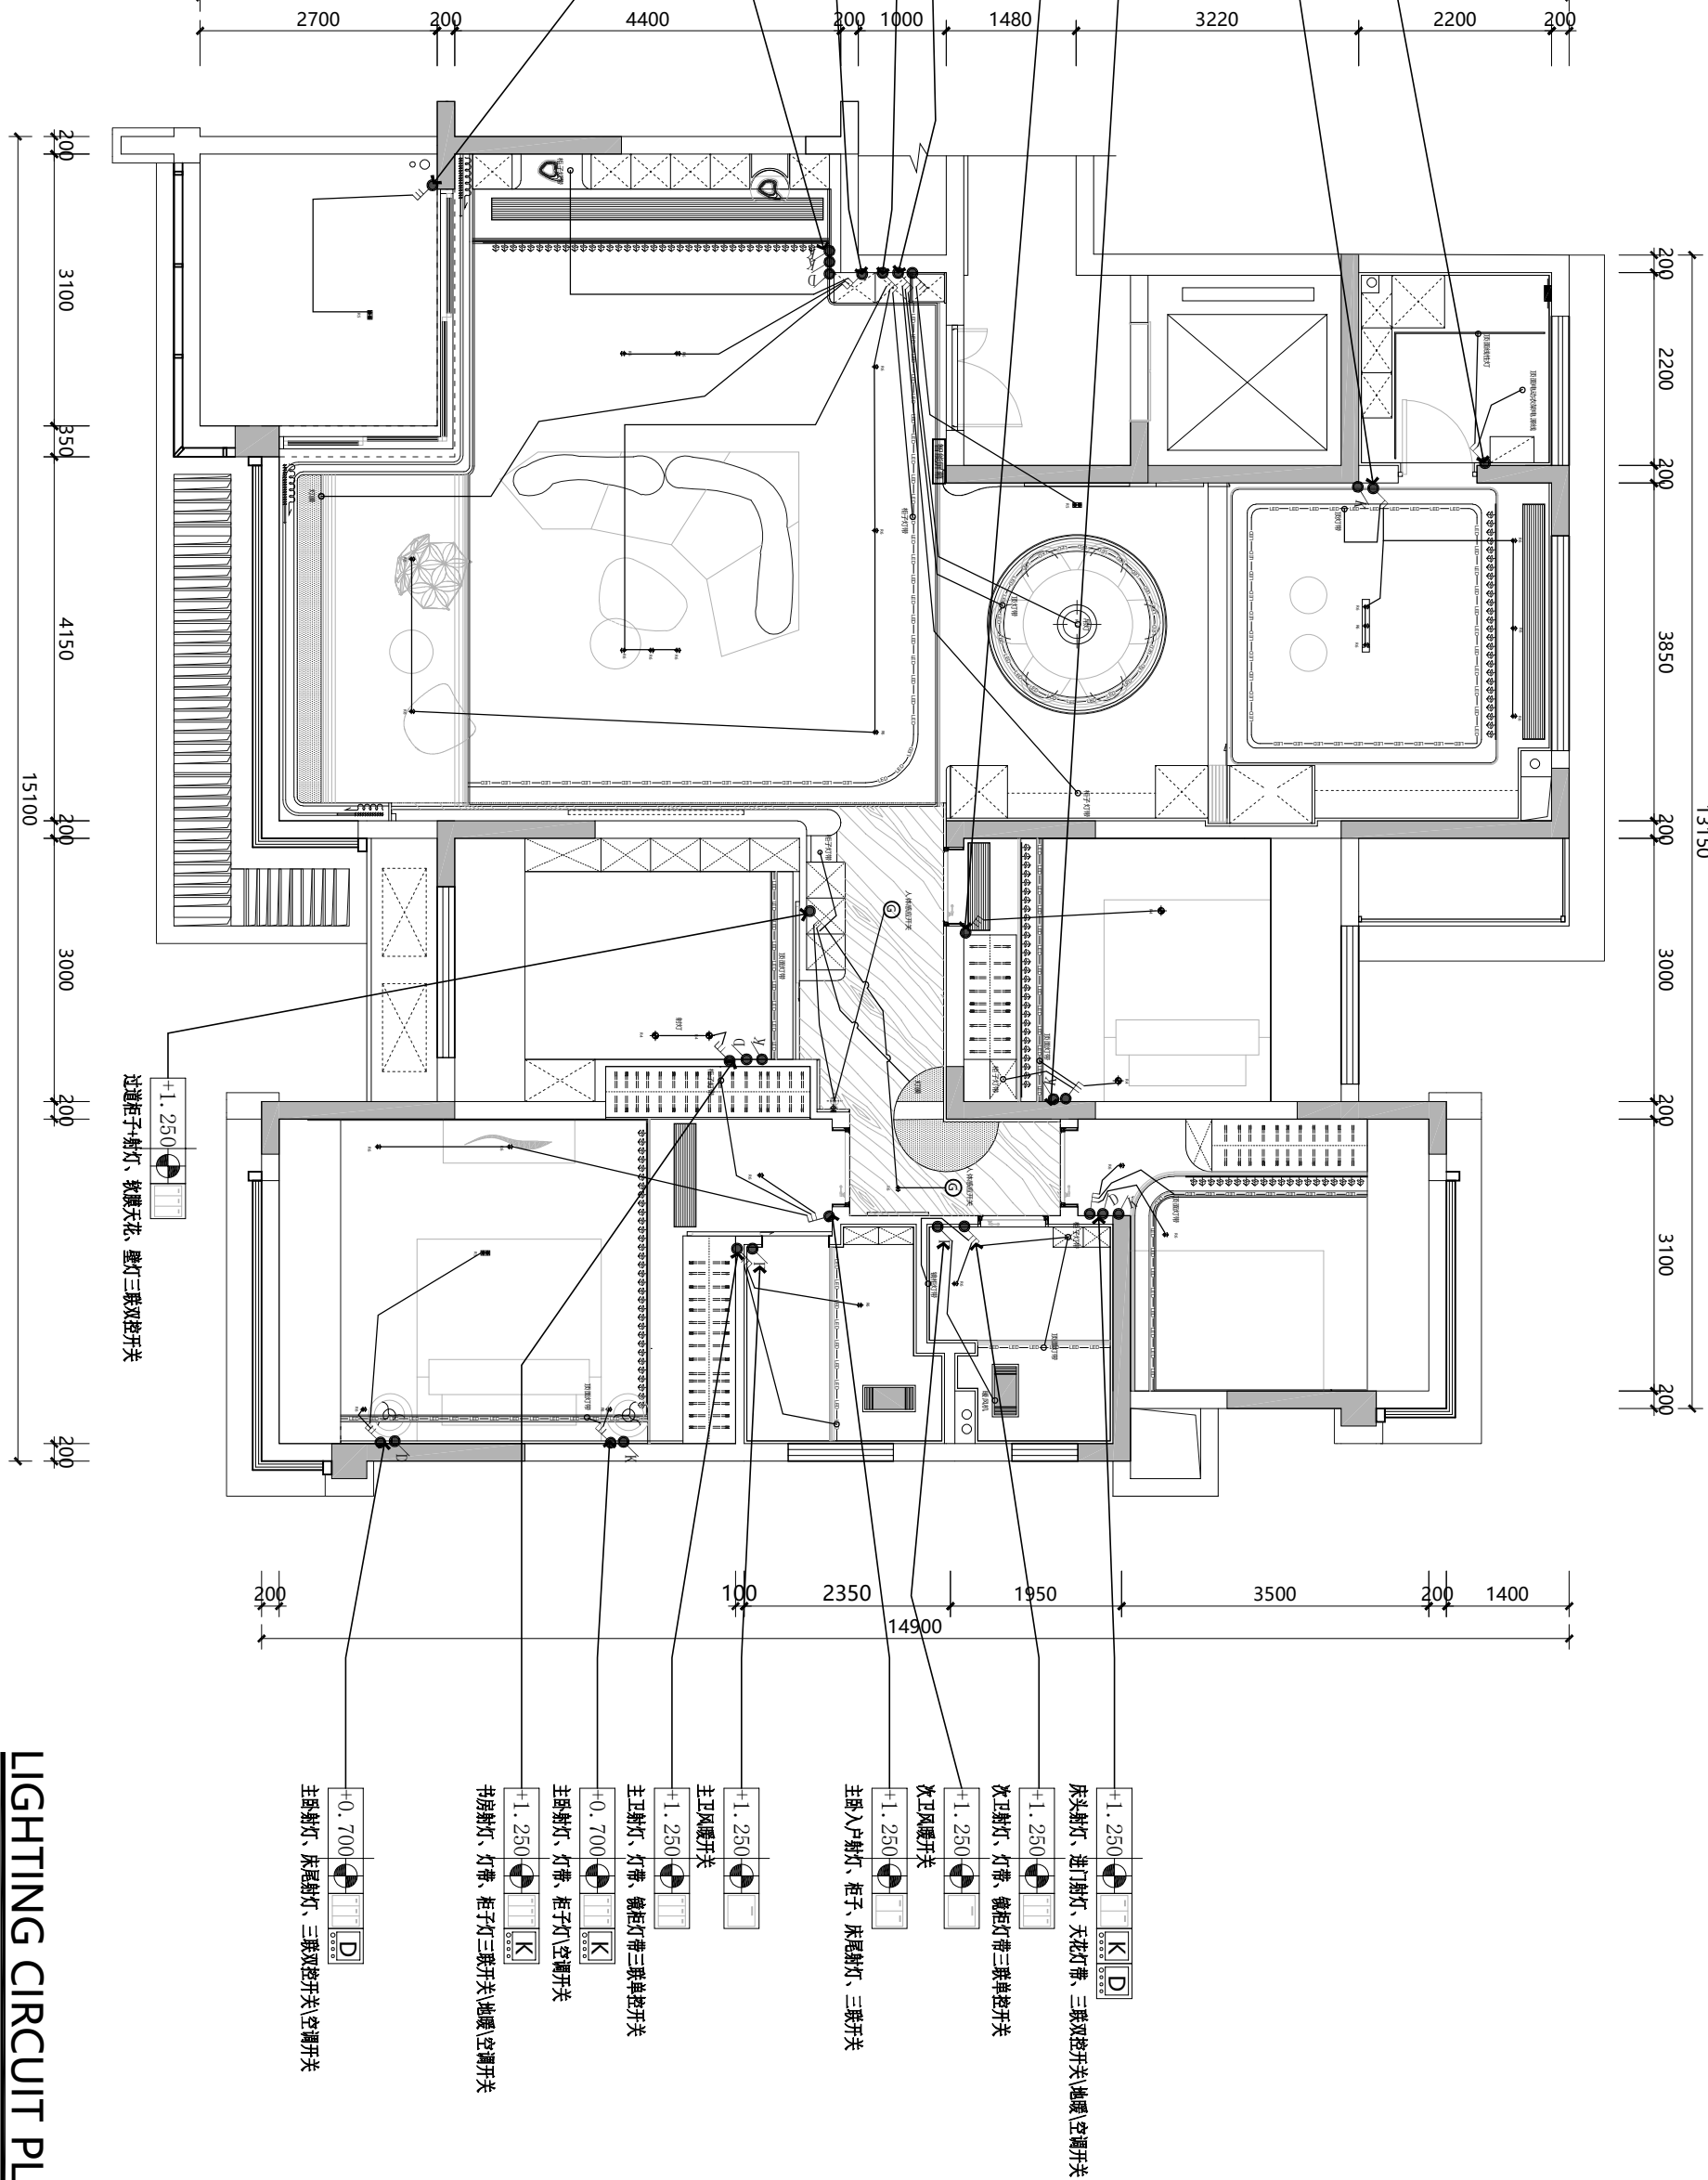

LIGHTING CIRCUIT PLAN
开关控制图
SCALE 1:80