



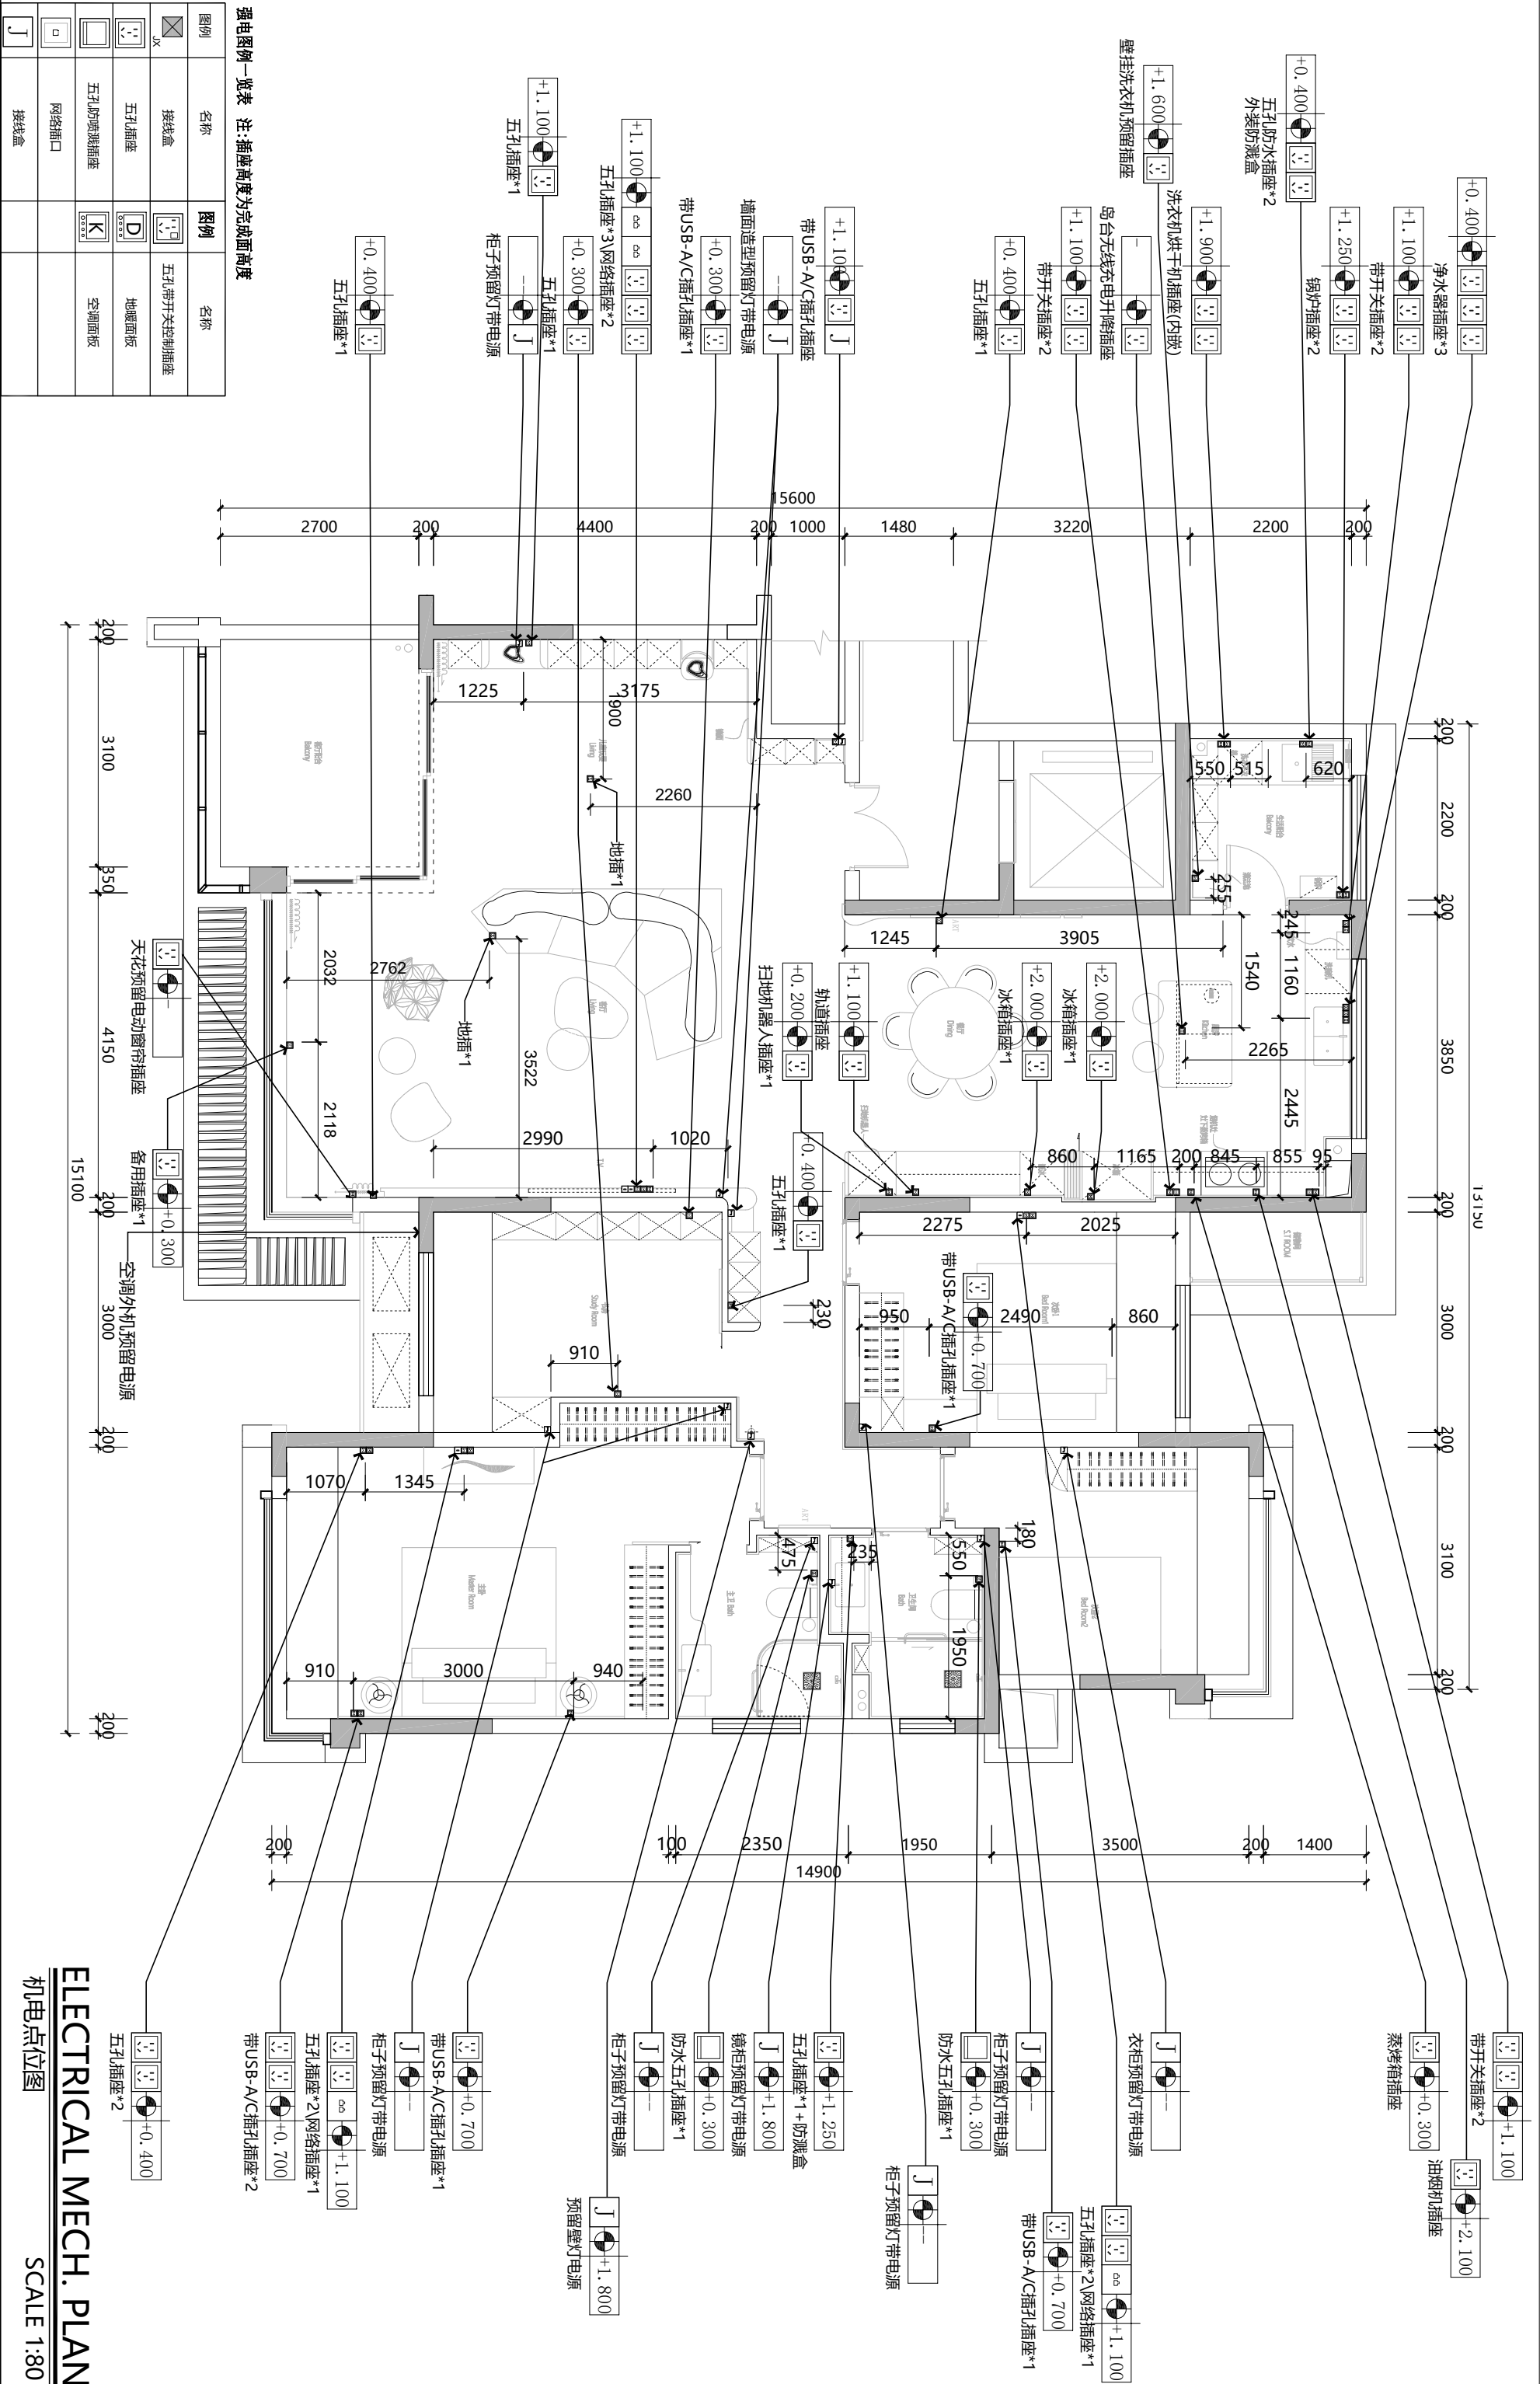

强电图例一览表 注:插座高度为完成面高度

图例	名称	图例	名称
	接线盒		五孔带开关控制插座
	五孔插座		地漏面板
	五孔防喷测插座		空调面板
	网络端口		
	接线盒		

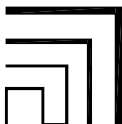

YS STUDIO
地址: 重庆市渝北区食品城大道创意公园4期7幢1单元2A

工程名称 PROJECT	昱湖壹号萃萃17-1-1502	编号 JOB NO		比例 SCALE	1:80	绘图 DRAWN BY	杨银兰	审核 APPROVED BY		图面修正 次别NO.		日期DATE	修改内容REVISION	图面修正 次别NO.		日期DATE	修改内容REVISION
图例 TITLE	机电点位图	日期 DATE	2025/2	单位 UNIT		设计 DESIGNED BY	杨银兰	核准 APPROVED BY		图面修正 次别NO.		日期DATE	修改内容REVISION	图面修正 次别NO.		日期DATE	修改内容REVISION

ELECTRICAL MECH. PLAN
机电点位图
SCALE 1:80

PL-06

页数 NUMBER
PL-06
版权所有
请尊重智慧财产权