


图例			
	双网格栅射灯		20瓦磁吸轨道灯
	方形可调射灯		伸缩可调射灯
	LED灯带		预埋线性LED灯
	可调嵌入式射灯		导轨射灯
	防水嵌入式射灯		阅读灯
	吸顶灯		吊灯
	筒灯		小射灯
	LED灯带		红外感应器
	平立面灯带		矩形筒形射灯
	电子LED灯		台灯
	预埋线性LED灯		夜灯
	长条形射灯		落地灯

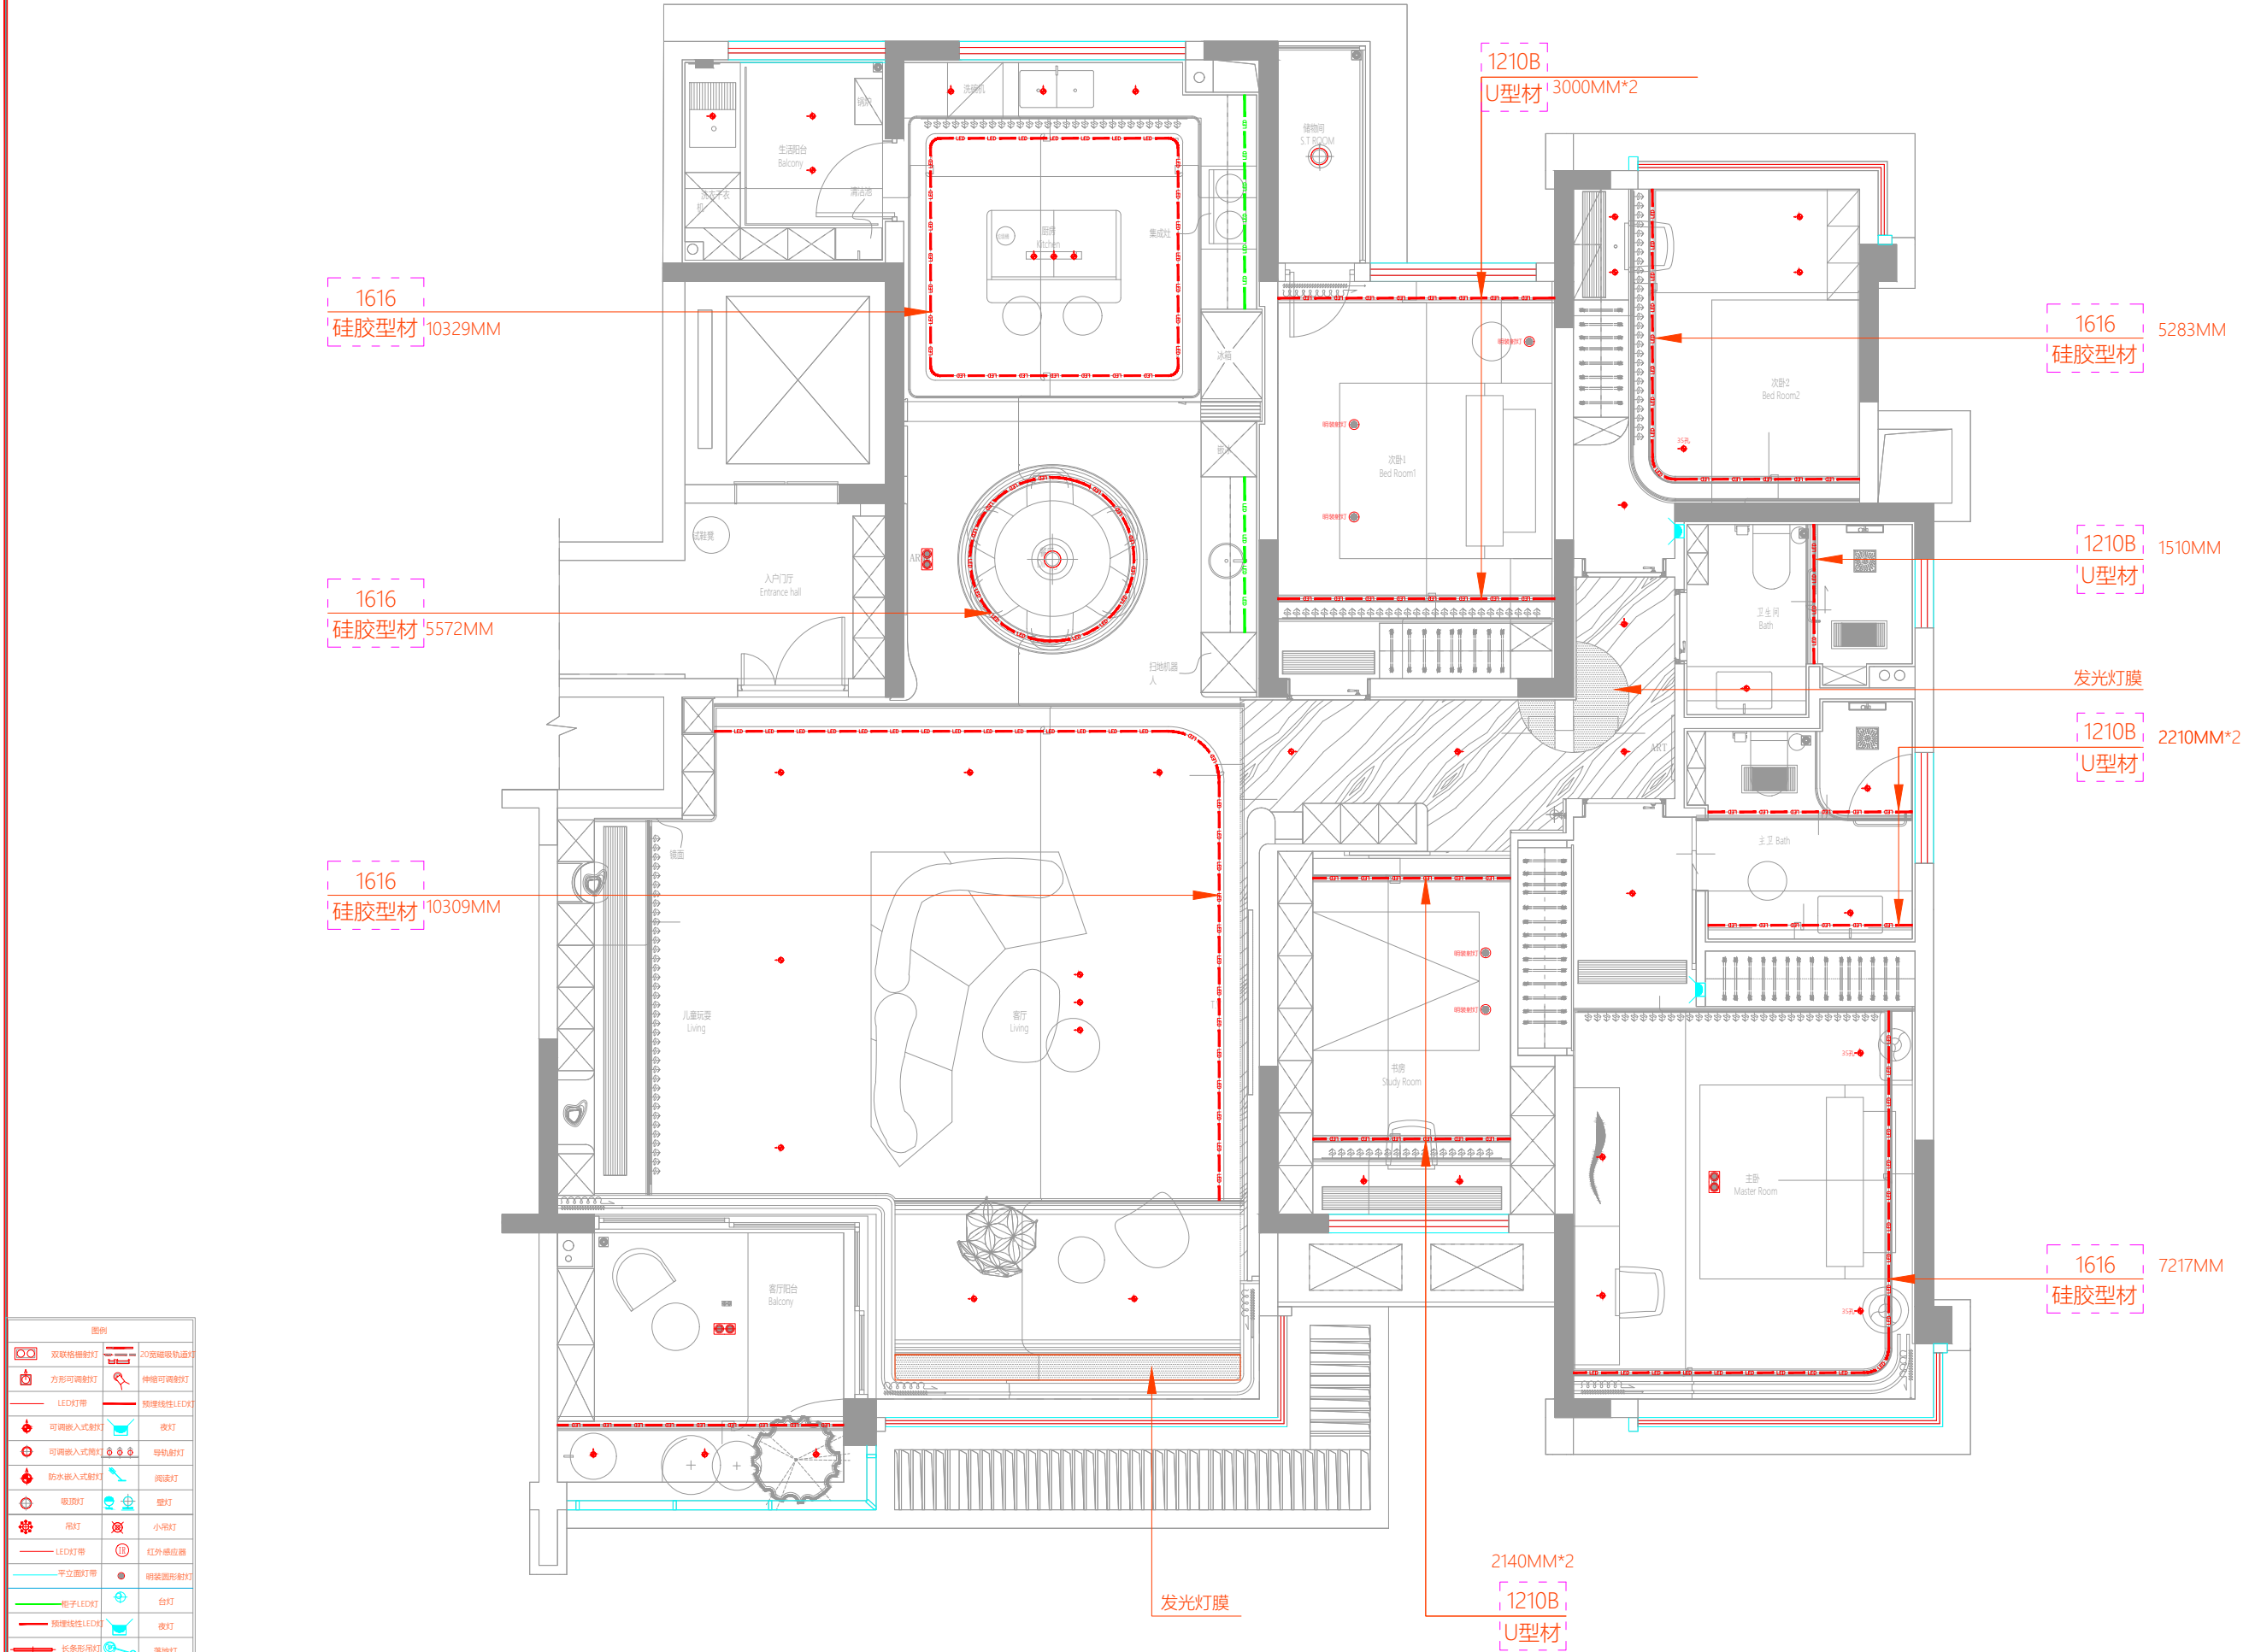

注；所有灯带均为低压灯带，变压器位置放置空调检修口。

NOTES:
注意：
施工单位及下属各工种应复核所有的现场尺寸，所有的图纸，节点图和详细说明书，如发现有出入应及时书面报告室内设计师

施工单位必须遵照所有的设计文件和材料，家具和灯具的性能要求，施工法规、条例。
我司提供给业主单位的所有图纸文件及书面材料均为我司的知识产权。未经允许，不得复印及

REVISION 修改:	DATE 日期:

CLIENT
客户已领悟图纸
确认签字:

PROJECT
工程名称:

昱湖壹号萃峯17-1-1502

DRAWING TITLE
图纸名称:

施工大样图

YS STUDIO

重庆设计YStudio

地址：重庆市渝北区食品大道创意公园17栋1单元24层

电话：18680966202

电话：135941459705

JOB NO. 项目编号:	
DATE 日期: 2024-07-11	THE CHIEF 项目组长: YS3
SCALE 比例:	DESIGNER 设计师: YS4
MAPAREA 图幅: A3	DRAWN 制图:
COMPERE 设计总监: YS1	APPROVED 审核: YS2
DWG NO. 图纸编号:	YS-P001

